


K.12.57.01.101

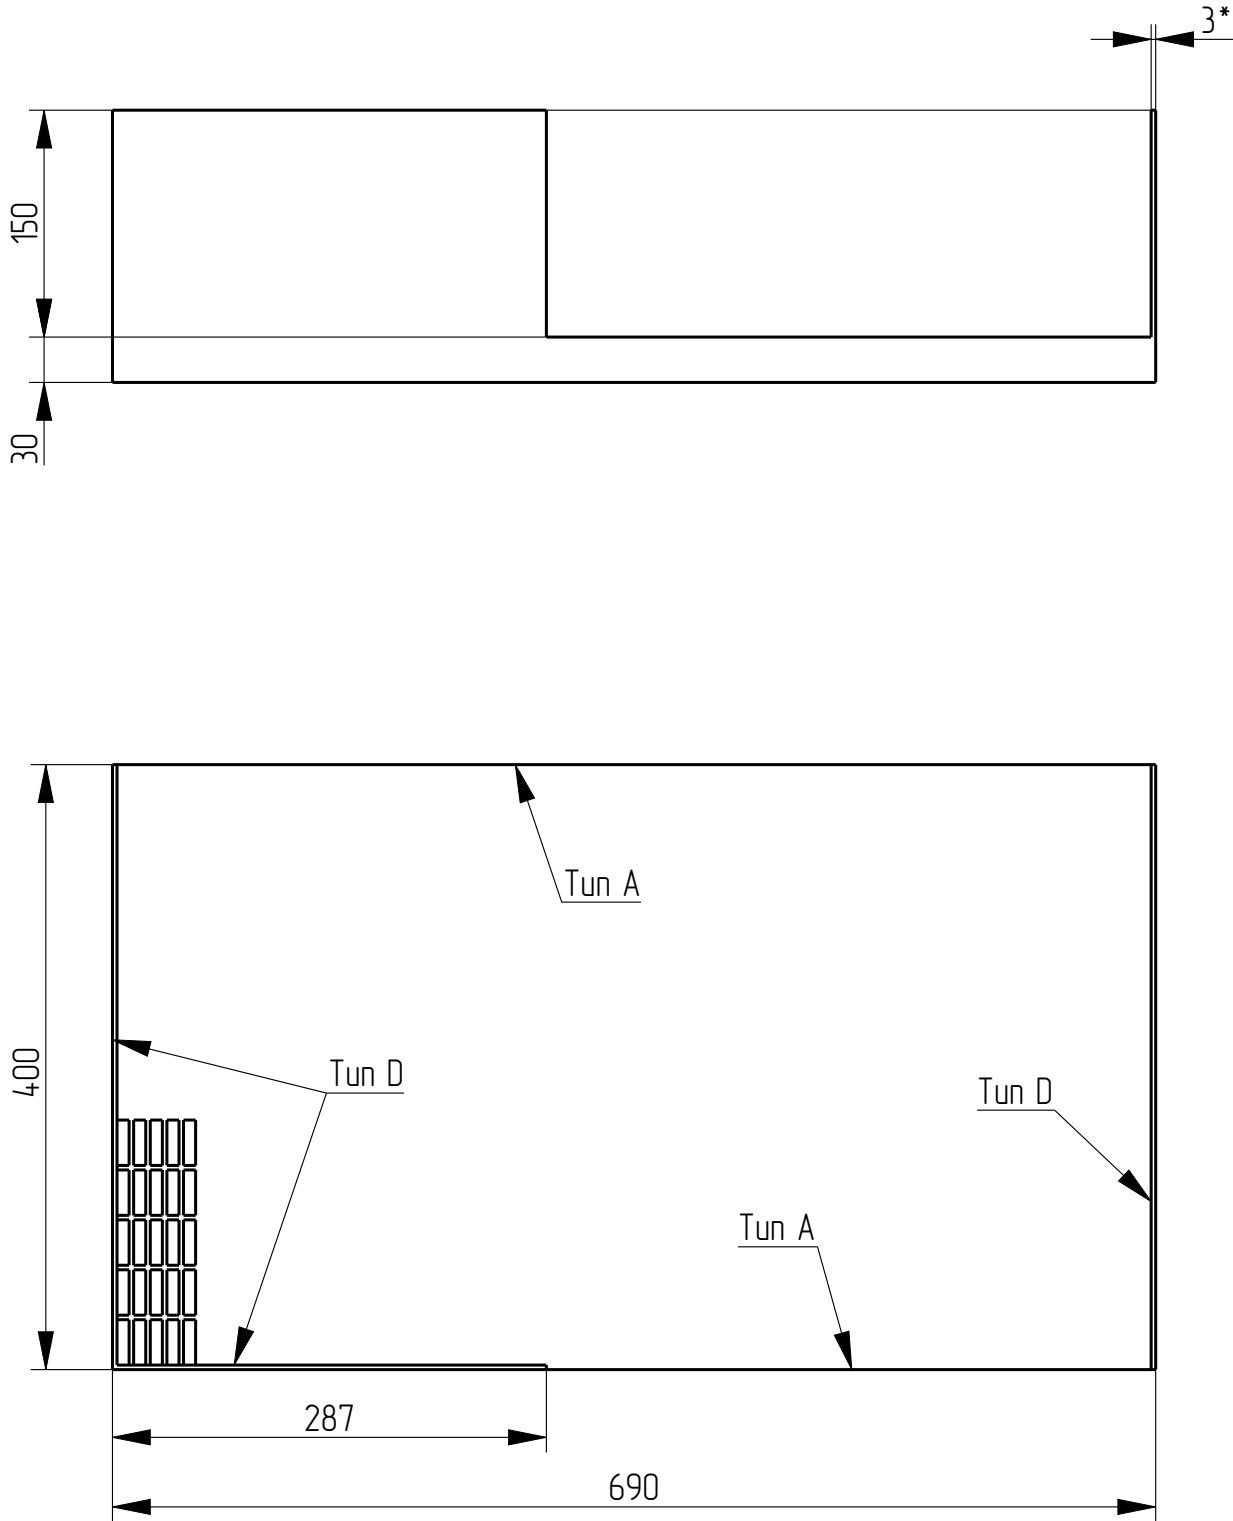

Характеристики настила	Значение
Тип настила	P
Тип зубьев противоскольжения	S1
Шаг несущих нагрузку полос, мм.	33
Шаг связующих полос, мм.	11
Высота несущей нагрузку полосы, мм.	30
Толщина несущей нагрузку полосы, мм.	3
Покрывтие решетки	Zn
Тип обрамления	см. эскиз
Толщина листа обрамления, мм.	3
Длина несущей нагрузку полосы, мм.	690
Ширина решетки (длина связующей полосы), мм.	400

- 1 *Размер для справок.
2 Общие допуски по ГОСТ 30893.1-2002: h16, $\pm$ IT16/2.
3 Маркировать обозначение чертежа.

					К.12.57.01.101					
					Настил	Лист			Масса	Масштаб
									11.6	1:5
Изм.	Лист	№ докум.	Подпись	Дата						
Разраб.										
Проб.										
Т. контр.						Лист			Листов	1
					Настил решетчатый Р 33х11/30х3 S1 Zn DIN24537					
Н. контр.										
Утв.										